

LEGENDA GERAL

- ELETRODUTO SUBINDO
- ELETRODUTO DESCENDO
- ELETRODUTO APARENTE
- ELETRODUTO EMBUTIDO NA PAREDE
- ELETRODUTO EMBUTIDO NO PISO
- TUBO CAMISA NA VIGA
- CAIXA DE PASSAGEM 4"x2" EMBUTIDA
- CAIXA DE PASSAGEM 4"x4" EMBUTIDA
- CAIXA DE PASSAGEM 4"x4" APARENTE
- CAIXA OCTOGONAL APARENTE
- QUADRO 1200x800x250 DE EMBUTIR/SOBREPOR
- TOMADA PARA TV
- TOMADA PARA MICROFONE
- PONTO DE INTERNET
- ALTO-FALANTE NO FORRO
- CONTROLE DE VOLUME NA PAREDE H=1,15m
- PEDESTAL MOTORIZADO

LEGENDA – RISCO NÍVEL 2

- SIRENE
- SENSOR DE MOVIMENTO INFRAVERMELHO, H=2,20m
- TECLADO DA CENTRAL DE ALARME, H=1,60m
- CÂMERA DOME NO FORRO
- CÂMERA EXTERNA

NOTAS

1. NOTAS GERAIS, ESPECIFICAÇÕES, DIAGRAMAS DE LIGAÇÃO, VER CADERNO DE DETALHES DE SISTEMAS DIGITAIS.

2. QUADRO DO BALCÃO DE ÁUDIO E VÍDEO, VER CADERNO DE DETALHES DE SISTEMAS DIGITAIS.

3. LAYOUT DOS ALTO–FALANTES NO FORRO, VER PLANTA DE ARQUITETURA.

4. USAR CURVAS LONGAS 90º NOS ELETRODUTOS RÍGIDOS.

5. EQUIPAMENTOS DE REDE DE DADOS: ROTEADOR WI–FI E SWITCH PoE. VER CADERNO DE DETALHES DE SISTEMAS DIGITAIS.


6. ALARME DE INTRUSÃO DO RISCO NÍVEL 2: CENTRAL DE ALARME, RECEPTOR, CONTROLE REMOTO, BATERIA, TECLADO, SENSORES INFRAVERMELHO INTERNOS E EXTERNOS, SIRENES, NOBREAK E FONTE 12V. PARA O NÍVEL 2, OS SENSORES INTERNOS E EXTERNOS SERÃO INSTALADOS COMO MOSTRADO NA PLANTA BAIXA FOLHA EY102. VER CADERNO DE DETALHES DE SISTEMAS DIGITAIS.

7. CFTV DO RISCO NÍVEL 2: GRAVADOR DIGITAL DE VÍDEO, VÍDEO POWER BALUN, CÂMERA DOME IP INTERNA E CÂMERAS EXTERNAS. PARA O NÍVEL 2, A CÂMERA DOME IP INTERNA E AS CÂMERAS EXTERNAS SERÃO INSTALADAS COMO MOSTRADO NA PLANTA BAIXA FOLHA EY102. PARA A INSTALAÇÃO DAS CÂMERAS CAM1 E CAM2 VER PLANTA DE CIVIL E CADERNO DE DETALHES DE SISTEMAS DIGITAIS.
8. QUADRO QC–1 DO RISCO NÍVEL 2: FAZER A INSTALAÇÃO DOS EQUIPAMENTOS CONFORME LAYOUT MOSTRADO NO CADERNO DE DETALHES DE SISTEMAS DIGITAIS. NECESSIDADE DE SEGUIR A POSIÇÃO DOS EQUIPAMENTOS CONFORME LAYOUT DO QC–1, PREVISÃO DE AMPLIAÇÃO PARA NÍVEL 3. O QUADRO DEVERÁ SER ATERRADADO.

9. CONTROLE DE ACESSO: FAZER APENAS A INFRAESTRUTURA PARA INTERFONE, FECHADURA ELÉTRICA DO PORTÃO DE PEDESTRES E DO MOTOR DO PORTÃO ELETRÔNICO. PARA A POSIÇÃO DAS CAIXAS DE PASSAGEM EXTERNAS, VER PLANTA DE CIVIL. ESTES EQUIPAMENTOS SOMENTE SERÃO ADQUIRIDOS PELA CONGREGAÇÃO APÓS VERIFICADA A NECESSIDADE JUNTAMENTE COM O LDC.
10. PARA DETALHES DE INFRAESTRUTURA, VER CADERNO DE DETALHES DE SISTEMAS DIGITAIS.

11. PROTEÇÃO PERIMETRAL PARA O RISCO NÍVEL 2: O SENSOR INFRAVERMELHO TIPO BARREIRA NÃO SERÁ INSTALADO, MAS A INFRAESTRUTURA SERÁ FEITA CONFORME NÍVEL 3., VER PLANTA DE CIVIL E CADERNO DE DETALHES DE SISTEMAS DIGITAIS.

12. PARA OS SISTEMAS DIGITAIS: APLICAR AS BOAS PRÁTICAS DE INSTALAÇÃO. USAR ELETRODUTO RÍGIDO DE ø1" PARA AS TUBULAÇÕES APARENTES ACIMA DO FORRO. OS ELETRODUTOS EMBUTIDOS TAMBÉM SERÃO DE ø1". OS ELETRODUTOS NO PISO SERÃO DO TIPO PEAD, USAR UNIDUTO CÔNICO, BUCHA E ARRUELA PARA CONEXÕES DE TUBULAÇÕES APARENTES COM CAIXAS DE PASSAGEM E QUÁDROS.

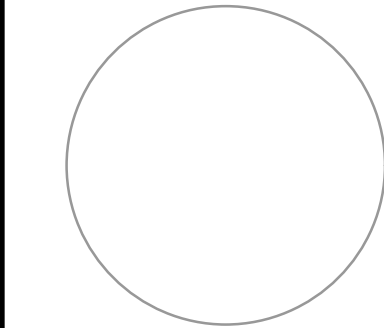

APROVADO PARA
CONSTRUÇÃO

FAVOR VERIFICAR TODAS DIMENSÕES NA OBRA
E RELATAR QUAISQUER DISCREPÂNCIAS

PLANTA REVISADA

DESTRUA TODAS CÓPIAS ENVIADAS ANTERIORMENTE

	17 DEZ 24	NÍVEL SEGURANÇA 2
–	30 NOV 23	APENAS C/ REFERENCIA
N.º:	DATA:	DESCRIÇÃO:

PROPRIETÁRIO:

N.º REGISTRO:

TÍTULO DO PROJETO:

SALÃO DO REINO

NOSSA SENHORA
DO SOCORRO/SE

TÍTULO DA FOLHA:


SISTEMAS DIGITAIS
LEGENDAS E NOTAS
NOTAS

N.º DO PROJETO:

BRA13126


N.º DA FOLHA:

EY001

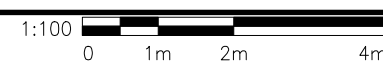


EY101

DATA PLOT: 17 dez 24
DIMSCALE: 1
CAMINHO ARQUIVO: C:\Users\afrei\Watchtower\Design - Projetistas Saloes do Reino\BRA13126-Nossa Senhora do Socorro-SE\5.Executivo\DIGIT\BRA13126 - EXE-EY.dwg

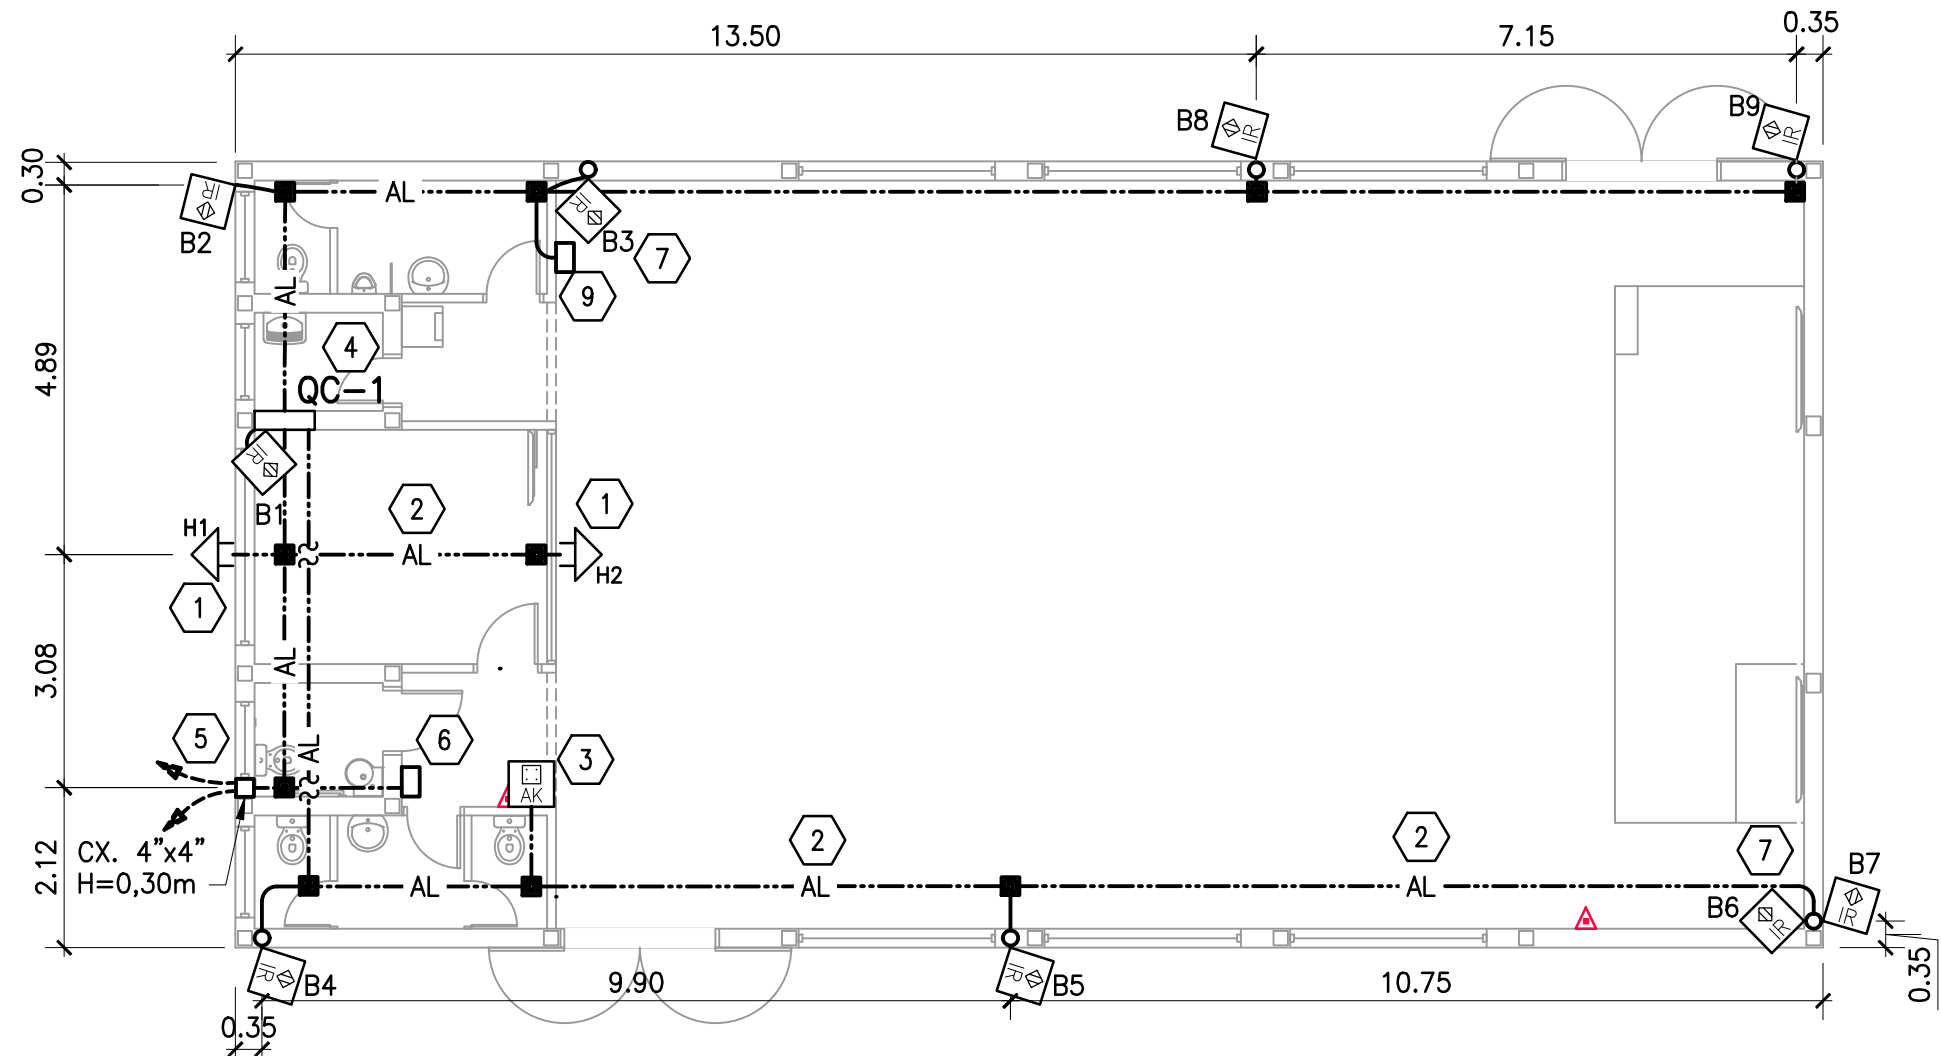

1 PLANTA BAIXA
SISTEMA DE ALARME DE INTRUSÃO

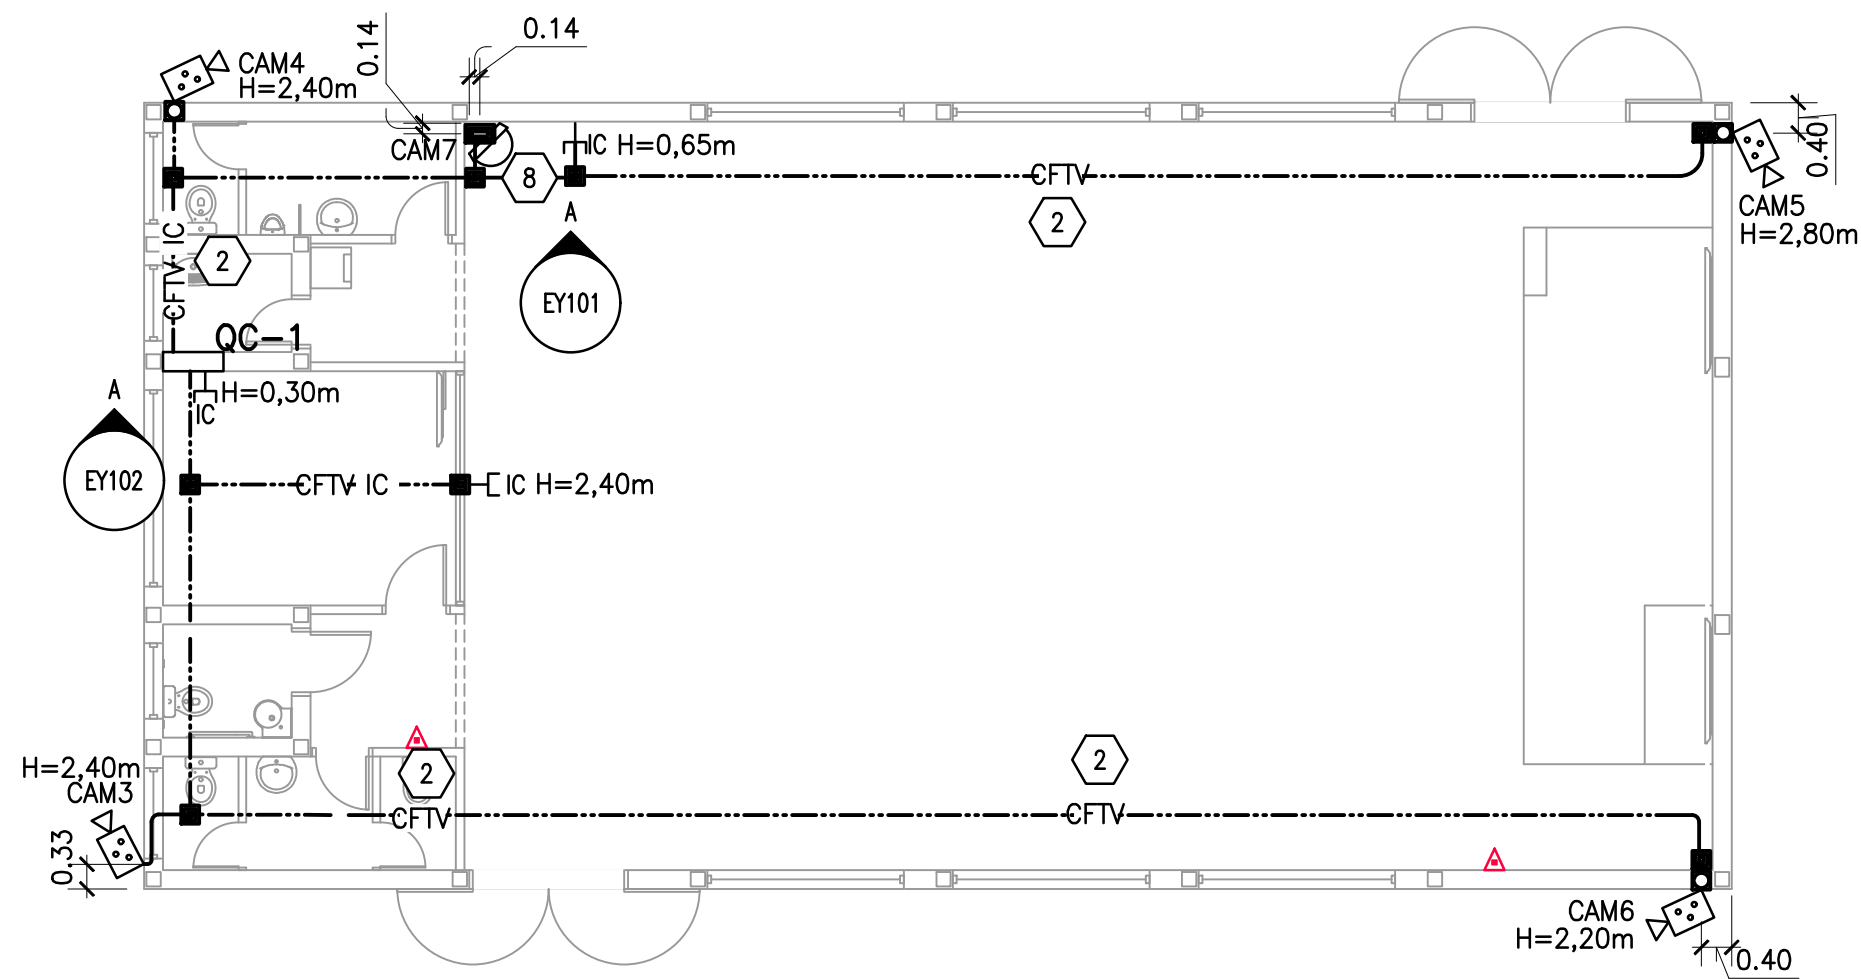


2 PLANTA BAIXA
SISTEMA DE CFTV E REDE DE DADOS



NOTAS-CHAVE

1. A SIRENE H1 DEVE SER INSTALADA EXTERNAMENTE, NA FACHADA FRONTAL DO SALÃO DO REINO, ABAIXO DO BEIRAL MAIS ELEVADO. A SIRENE H2 DEVE SER INSTALADA INTERNAMENTE, ACIMA DO FORRO DA SALA DE REUNIÃO.
2. ELETRODUTOS DO SISTEMA DE ALARME DE INTRUSÃO, CFTV E REDE DE DADOS É DE $\phi 1"$.
3. TECLADO DA CENTRAL DE ALARME, H=1,60m.
4. QUADRO 1200x800x250, CENTRAL DE SEGURANÇA (QC-1), H=1,80m.
5. VAI PARA CÂMERAS EXTERNAS CAM1 E CAM2. APENAS INFRAESTRUTURA: SENSOR INFRAVERMELHO BARREIRA, INTERFONE, FECHADURA ELÉTRICA E COMANDO MOTOR PORTÃO ELETRÔNICO. VER FOLHA DE CIVIL E CADERNO DE DETALHES DE SISTEMAS DIGITAIS.
6. APENAS INFRAESTRUTURA, CAIXA 4"x2" PREVISTA PARA INTERFONE, H=1,60m.
7. CONECTAR NA RÉGUA DE BORNE OS SENSORES INTERNOS EM SÉRIE NA MESMA ZONA, VER CADERNO DE DETALHES DE SISTEMAS DIGITAIS.
8. CAM7: VISÃO DO AUDITÓRIO. CÂMERA DOME INSTALADA ABAIXO DO FORRO.
9. CAIXA 4"x2" PARA RECEPTOR DA CENTRAL DE ALARME, H=2,40m.
10. PONTO DE TOMADA RJ45, H=0,30m. APENAS INFRAESTRUTURA: CAIXA 4"x2" PARA TOMADA TELEFÔNICA RJ11, H=0,30m.
11. APENAS INFRAESTRUTURA, ELETRODUTO PARA A ALIMENTAÇÃO ELÉTRICA DO INTERFONE PREVISTO.
12. PARA O PONTO IC NO BALCÃO DE ÁUDIO E VÍDEO NÃO HAVERÁ TOMADA RJ45, CRIMPAR O CABO DE REDE PARA CONEXÃO DIRETA COM O EQUIPAMENTO.

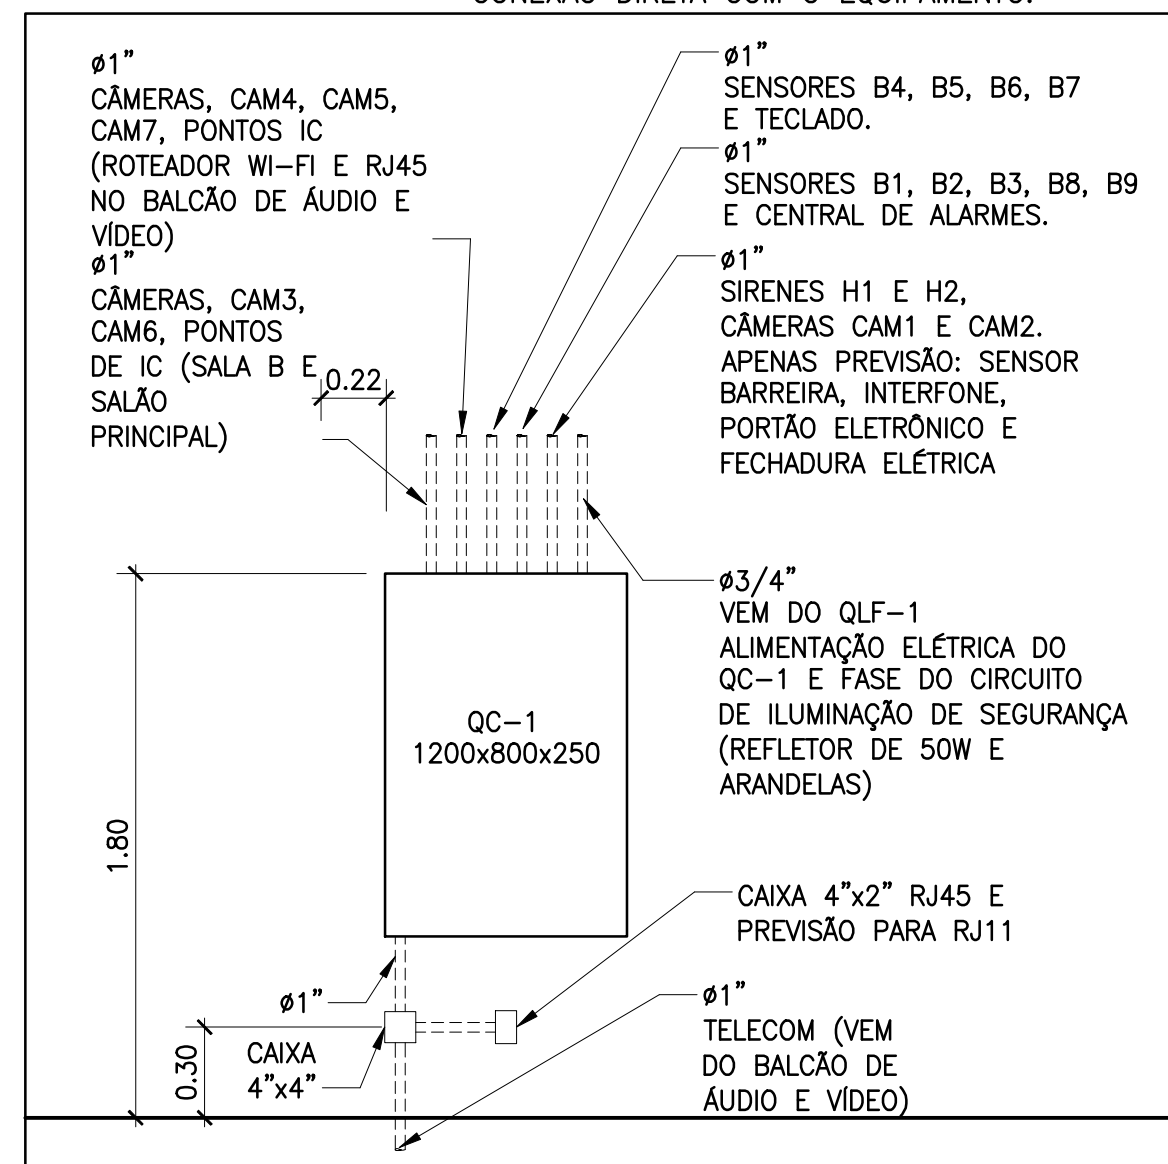

A ELEVÇÃO
QUADRO QC-1



APROVADO PARA CONSTRUÇÃO

FAVOR VERIFICAR TODAS DIMENSÕES NA OBRA
E RELATAR QUAISQUER DISCREPÂNCIAS

PLANTA REVISADA

DESTRUA TODAS CÓPIAS ENVIADAS ANTERIORMENTE

17 DEZ 24	NÍVEL SEGURANÇA 2
30 NOV 24	APENAS C/ REFERENCIA
N.º:	DATA:
	DESCRIÇÃO:

PROPRIETÁRIO:

N.º REGISTRO:

TÍTULO DO PROJETO:

SALÃO DO REINO

NOSSA SENHORA
DO SOCORRO/SE

TÍTULO DA FOLHA:

**NÍVEL 2-ALARME DE INTRUSÃO,
CFTV, REDE DE DADOS E QC-1
PLANTAS BAIXAS E ELEVÇÃO**

N.º DO PROJETO:

BRA13126

N.º DA FOLHA:

EY102